LEYENDA:

- Muros
- Vigas
- Muros invertidos

COMENTARIOS:

MUROS:
Todos los muros en el primer piso tienen un espesor de 25 cm.

VIGAS:
Se encuentran 3 tipos de viga:
1.- (25 / 74) cm (invertida) ubicada en la fachada del edificio
2.- (25 / 164) cm (invertida) ubicada en la fachada del edificio
3.- (25 / 72) cm (invertida) ubicada en la caja escala del edificio

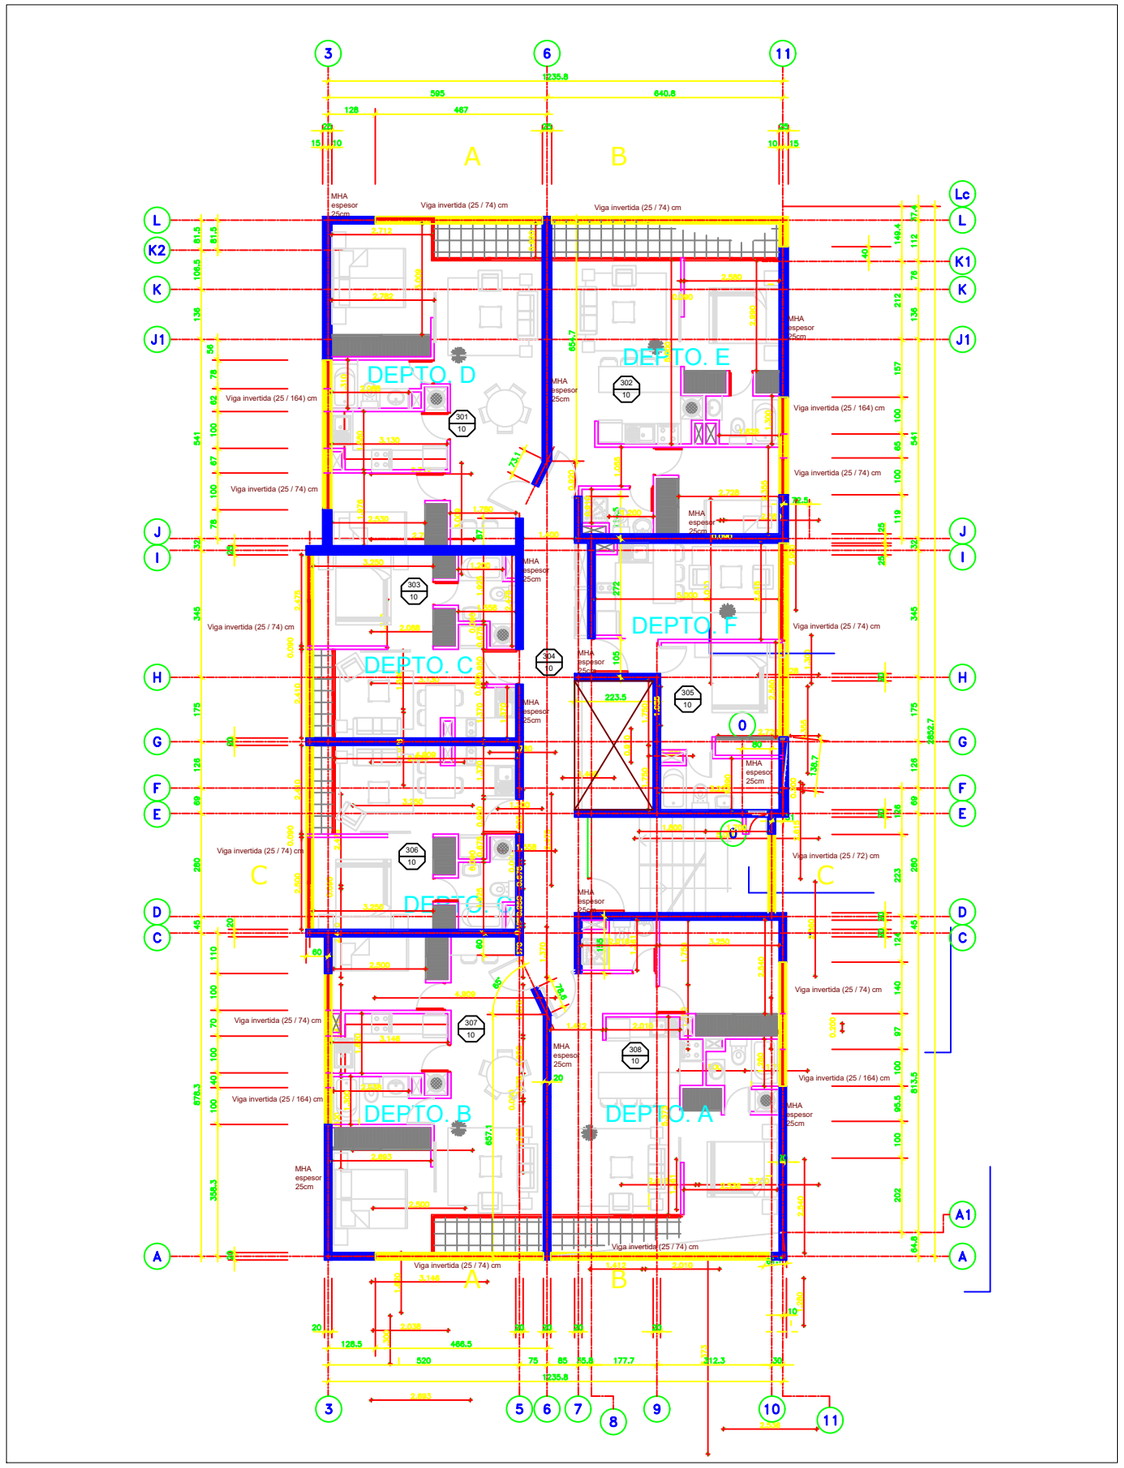

Universidad de los Andes > FACULTAD DE INGENIERÍA Y CIENCIAS APLICADAS	TRABAJO 2: ESTRUCTURACIÓN Y PRECALCULO SÍSMICO		REVISIÓN	FECHA	DESCRIPCIÓN DE LA REVISIÓN
			A	15/04/2026	Para revisión de profesor
PROYECTO CIVIL 202610-6102	**PLANOS DE ESTRUCTURACION**				
Proyectó: Grupo 1 / Fecha: Abril 2026	Planos de: Planta Piso 3° - tipo				
PLANO N°4 DE 4	NUMERO DIBUJO T_A - 01	REV. A			