LEYENDA:

- Muros
- Vigas
- Muros invertidos

COMENTARIOS:

MUROS:
Todos los muros en el primer piso tienen un espesor de 25 cm.

VIGAS:
Se encuentran 3 tipos de viga:
1.- (25 / 74) cm (invertida) ubicada en la fachada del edificio
2.- (25 / 164) cm (invertida) ubicada en la fachada del edificio
3.- (25 / 72) cm (invertida) ubicada en la caja escala del edificio

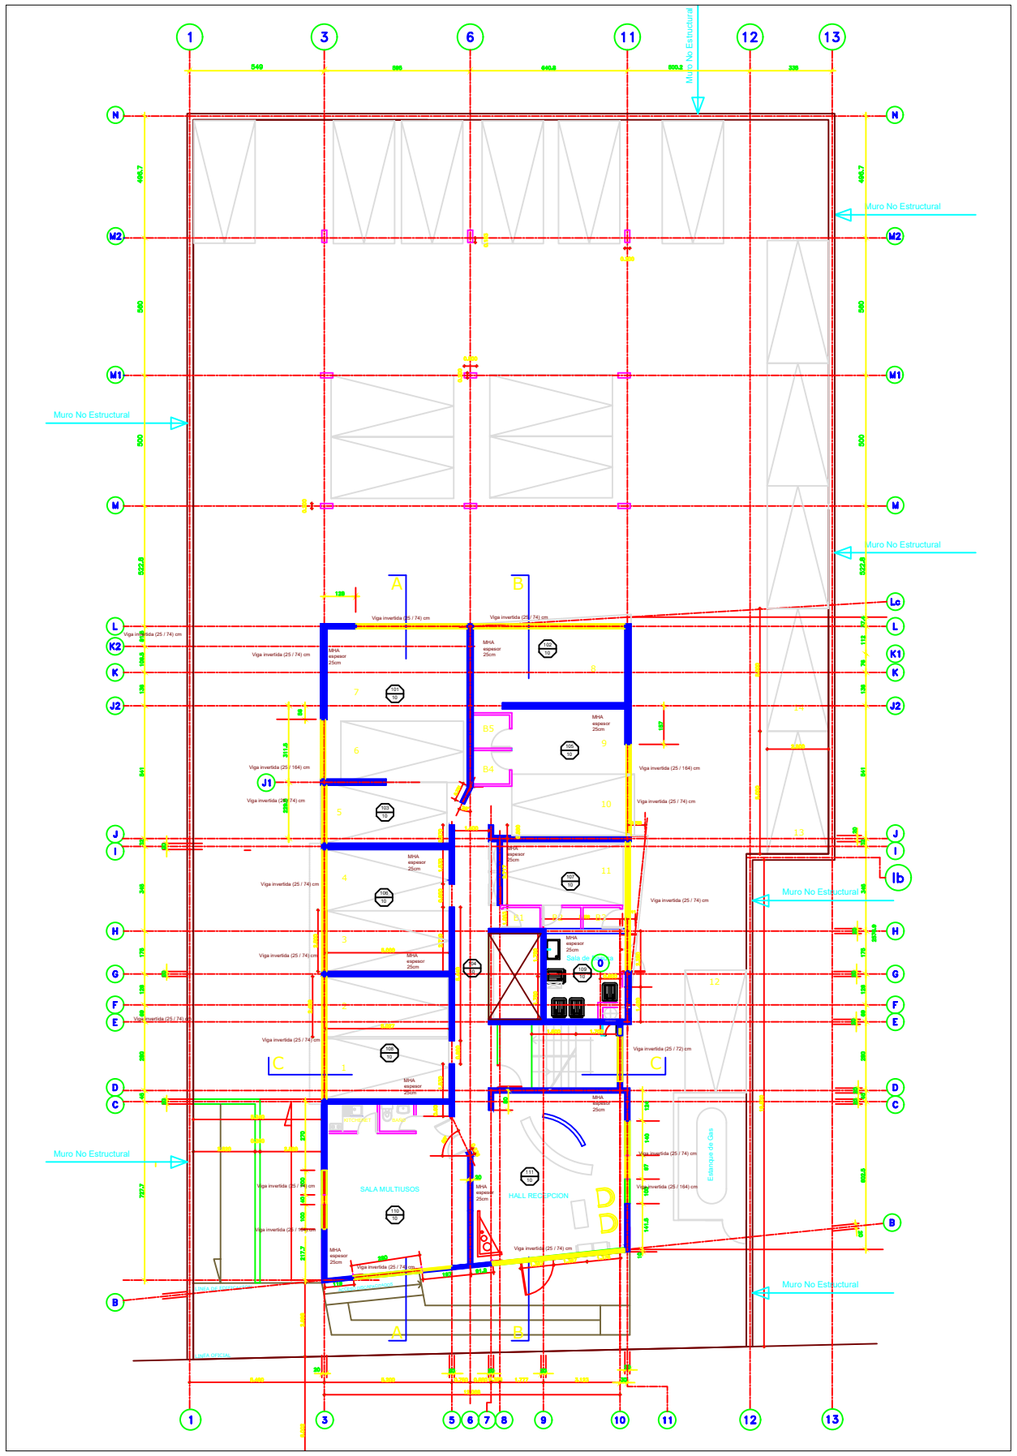

Universidad de los Andes > FACULTAD DE INGENIERIA Y CIENCIAS APLICADAS		TRABAJO 2: ESTRUCTURACIÓN Y PRECALCULO SÍSMICO		REVISIÓN	FECHA	DESCRIPCIÓN DE LA REVISIÓN
				A	15/04/2026	Para revisión de profesor
PROYECTO CIVIL 202610-6102		**PLANOS DE ESTRUCTURACION**				
Proyectó: Grupo 1	Fecha: Abril 2026	Planos de: Planta Piso 1°				
	PLANO N°2 DE 4		REV. A			