LEYENDA:

- Muros
- Vigas
- Muros invertidos

COMENTARIOS:

MUROS:
Todos los muros en el subterráneo tienen un espesor de 25 cm.

VIGAS:
En el subterráneo se encuentran solo vigas (25 / 50) cm.

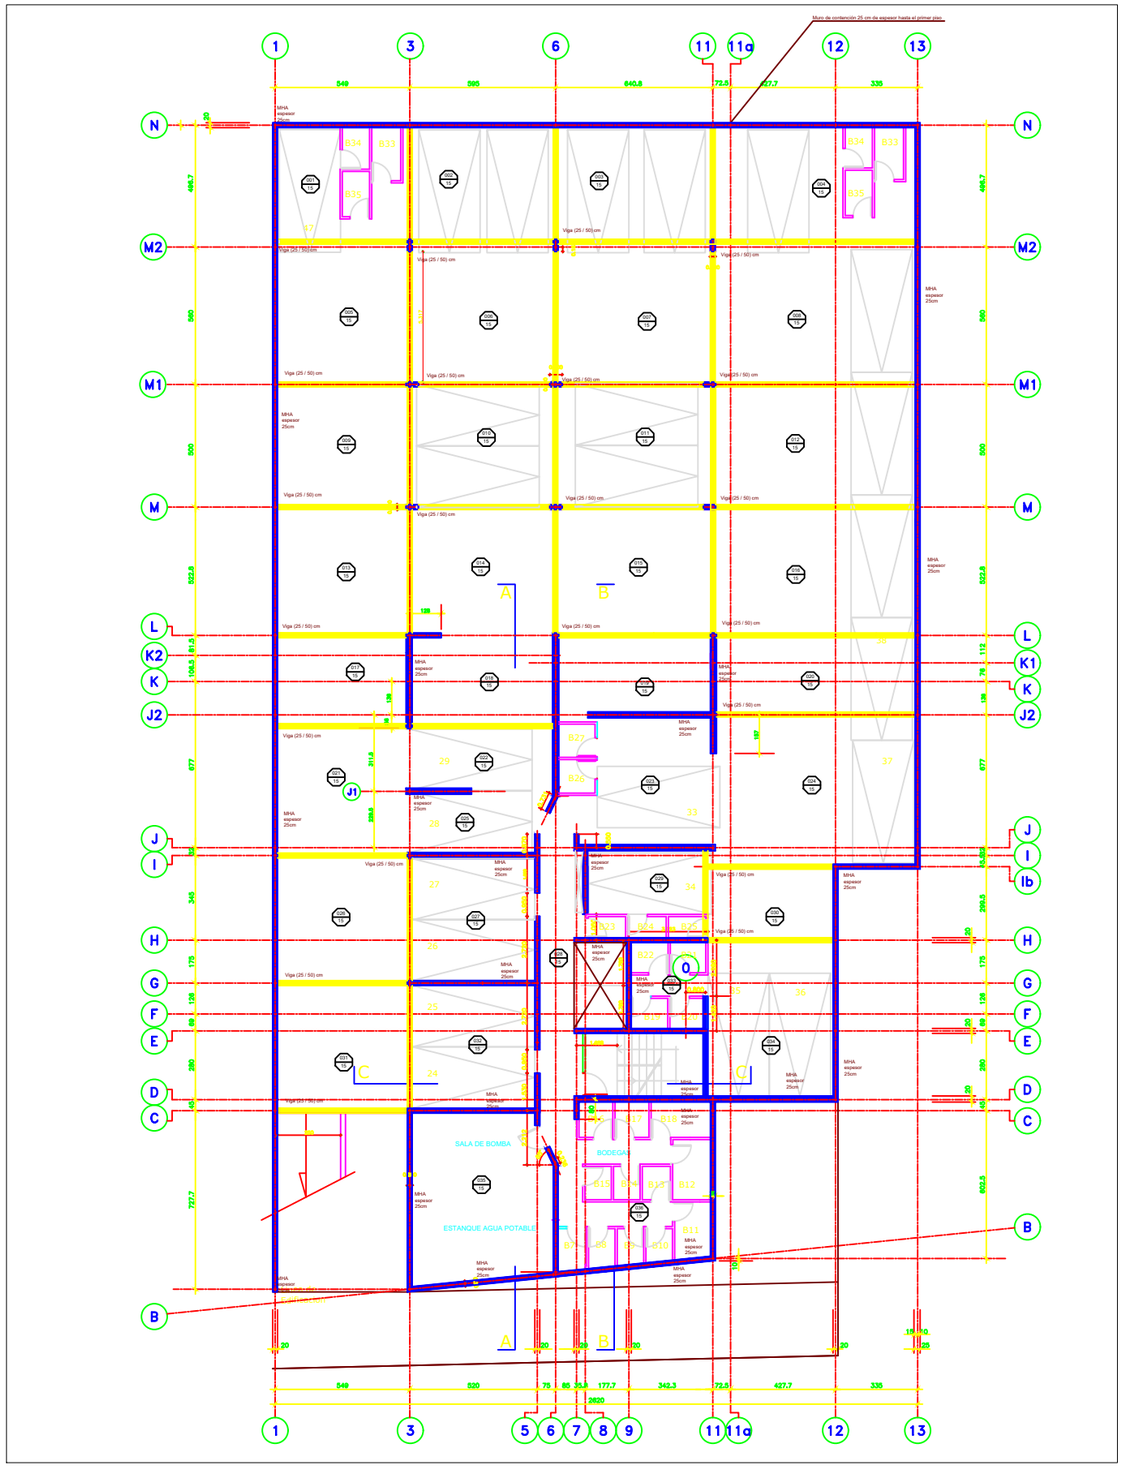

Universidad de los Andes > FACULTAD DE INGENIERÍA Y CIENCIAS APLICADAS	TRABAJO 2: ESTRUCTURACIÓN Y PRECALCULO SÍSMICO		REVISIÓN	FECHA	DESCRIPCIÓN DE LA REVISIÓN
			A	15/04/2026	Para revisión de profesor
PROYECTO CIVIL 202610-6102	**PLANOS DE ESTRUCTURACION**				
Proyectó: Grupo 1 / Fecha: Abril 2026	Planos de: Planta Subterráneo				
PLANO N°1 DE 4		REV. A			