

LEYENDA:

Muros


Vigas

Muros invertidos

COMENTARIOS:

MUROS:
Todos los muros en el primer piso tienen un espesor de 25 cm.

VIGAS:
Se encuentran 3 tipos de viga:
1.- V 25 / 74 cm (invertida) ubicada en la fachada del edificio
2.- V 25 / 164 cm (invertida) ubicada en la fachada del edificio
3.- V 25 / 72 cm (invertida) ubicada en la caja escala del edificio
4.- V 25 / 30 cm (normal) ubicada en la losa 101

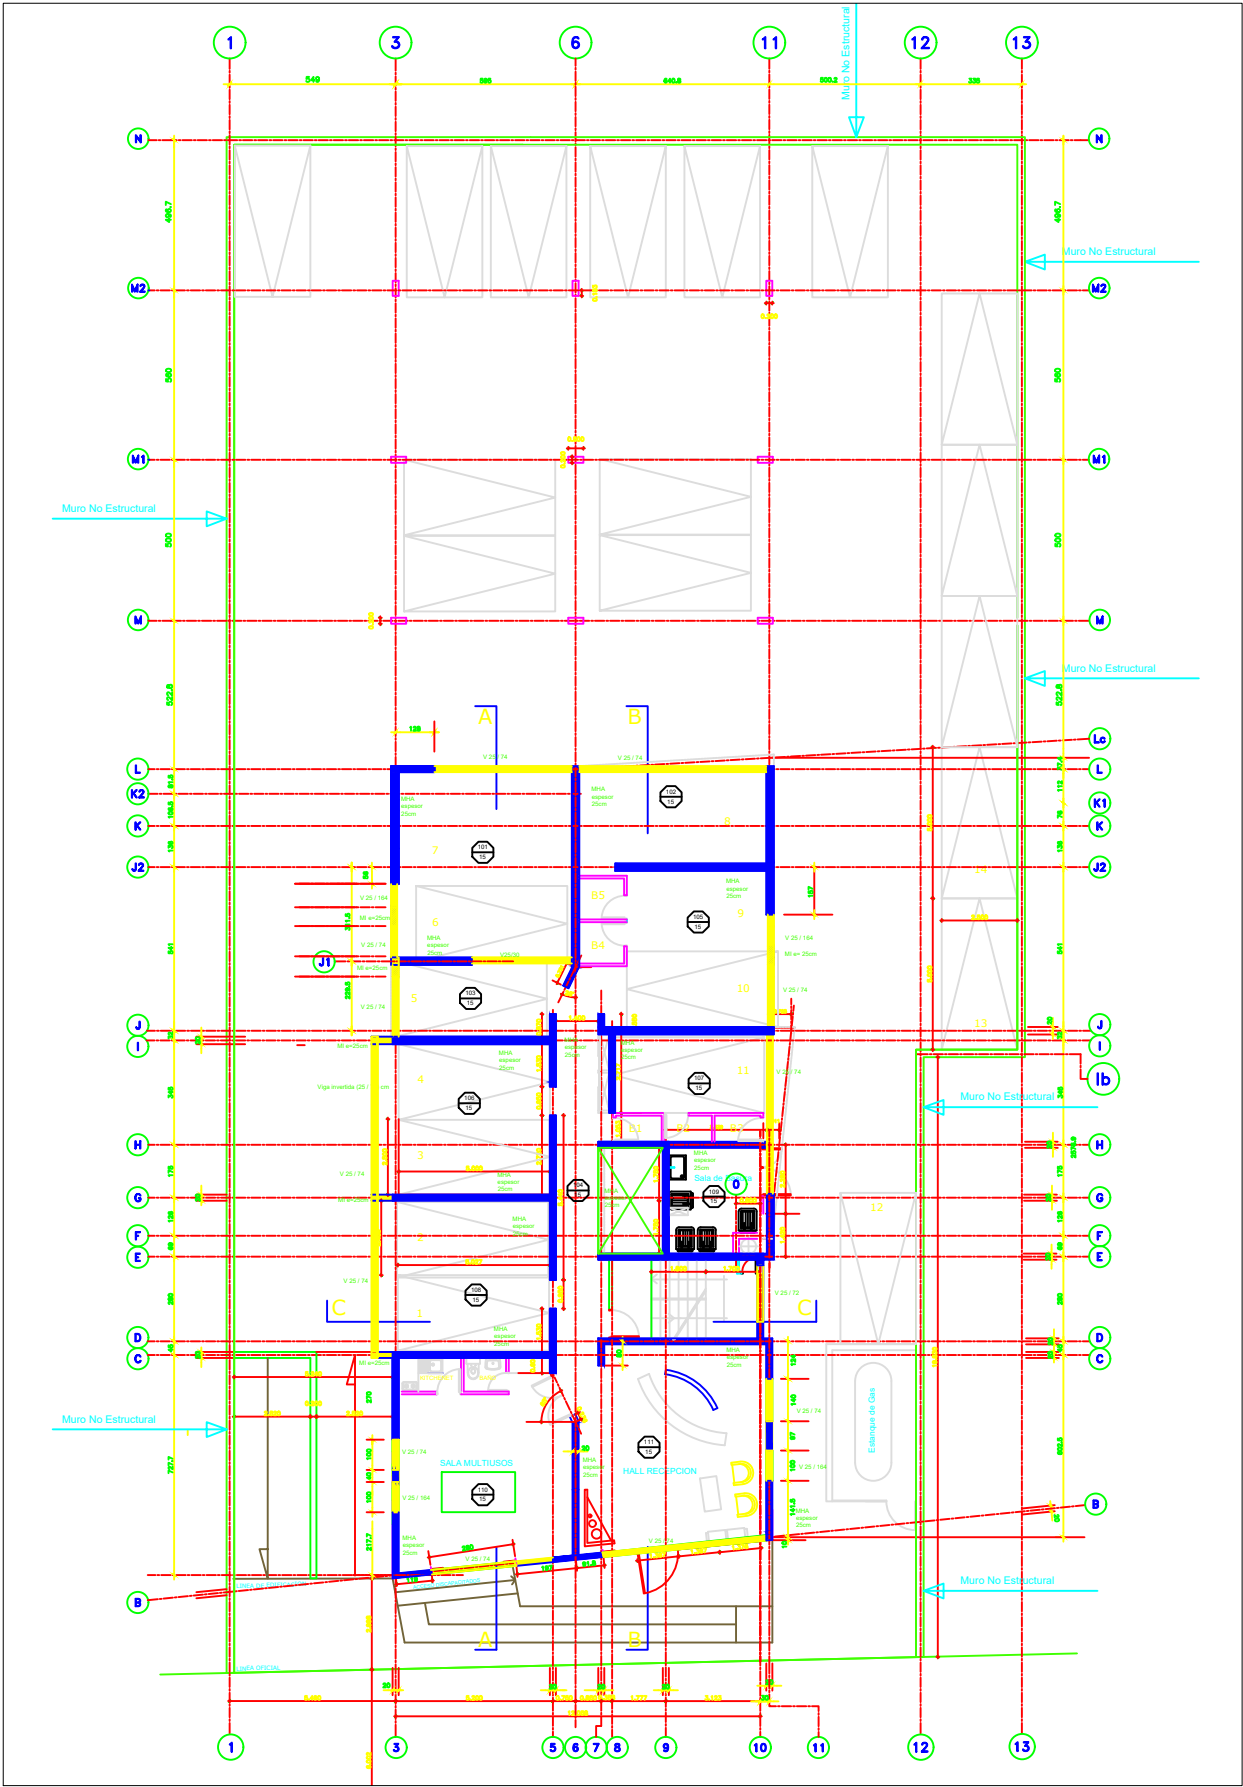

Universidad de los Andes FACULTAD DE INGENIERIA Y CIENCIAS APLICADAS		TRABAJO 2: ESTRUCTURACIÓN Y PRECÁLCULO SÍSMICO PLANOS DE ESTRUCTURACION Planos de: Planta Piso 1*		REVISIÓN	FECHA	DESCRIPCIÓN DE LA REVISIÓN
PROYECTO CIVIL 202610-6102				A	15/04/2026	Para revisión de profesor
Proyectó: Grupo 1	Fecha: Abril 2026					
	PLANO N°2 DE 4			REV. A		