


LEYENDA:

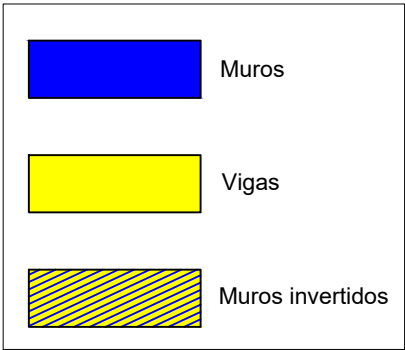

COMENTARIOS:


MUROS:

Todos los muros en el primer piso 3 tienen un espesor de 25 cm de el 4 hasta el último tienen un espesor de 20cm

VIGAS:

Se encuentran 3 tipos de viga:

- 1.- V 25 / 74 cm (invertida) ubicada en la fachada del edificio
- 2.- V 25 / 164 cm (invertida) ubicada en la fachada del edificio
- 3.- V 25 / 72 cm (invertida) ubicada en la caja escala del edificio

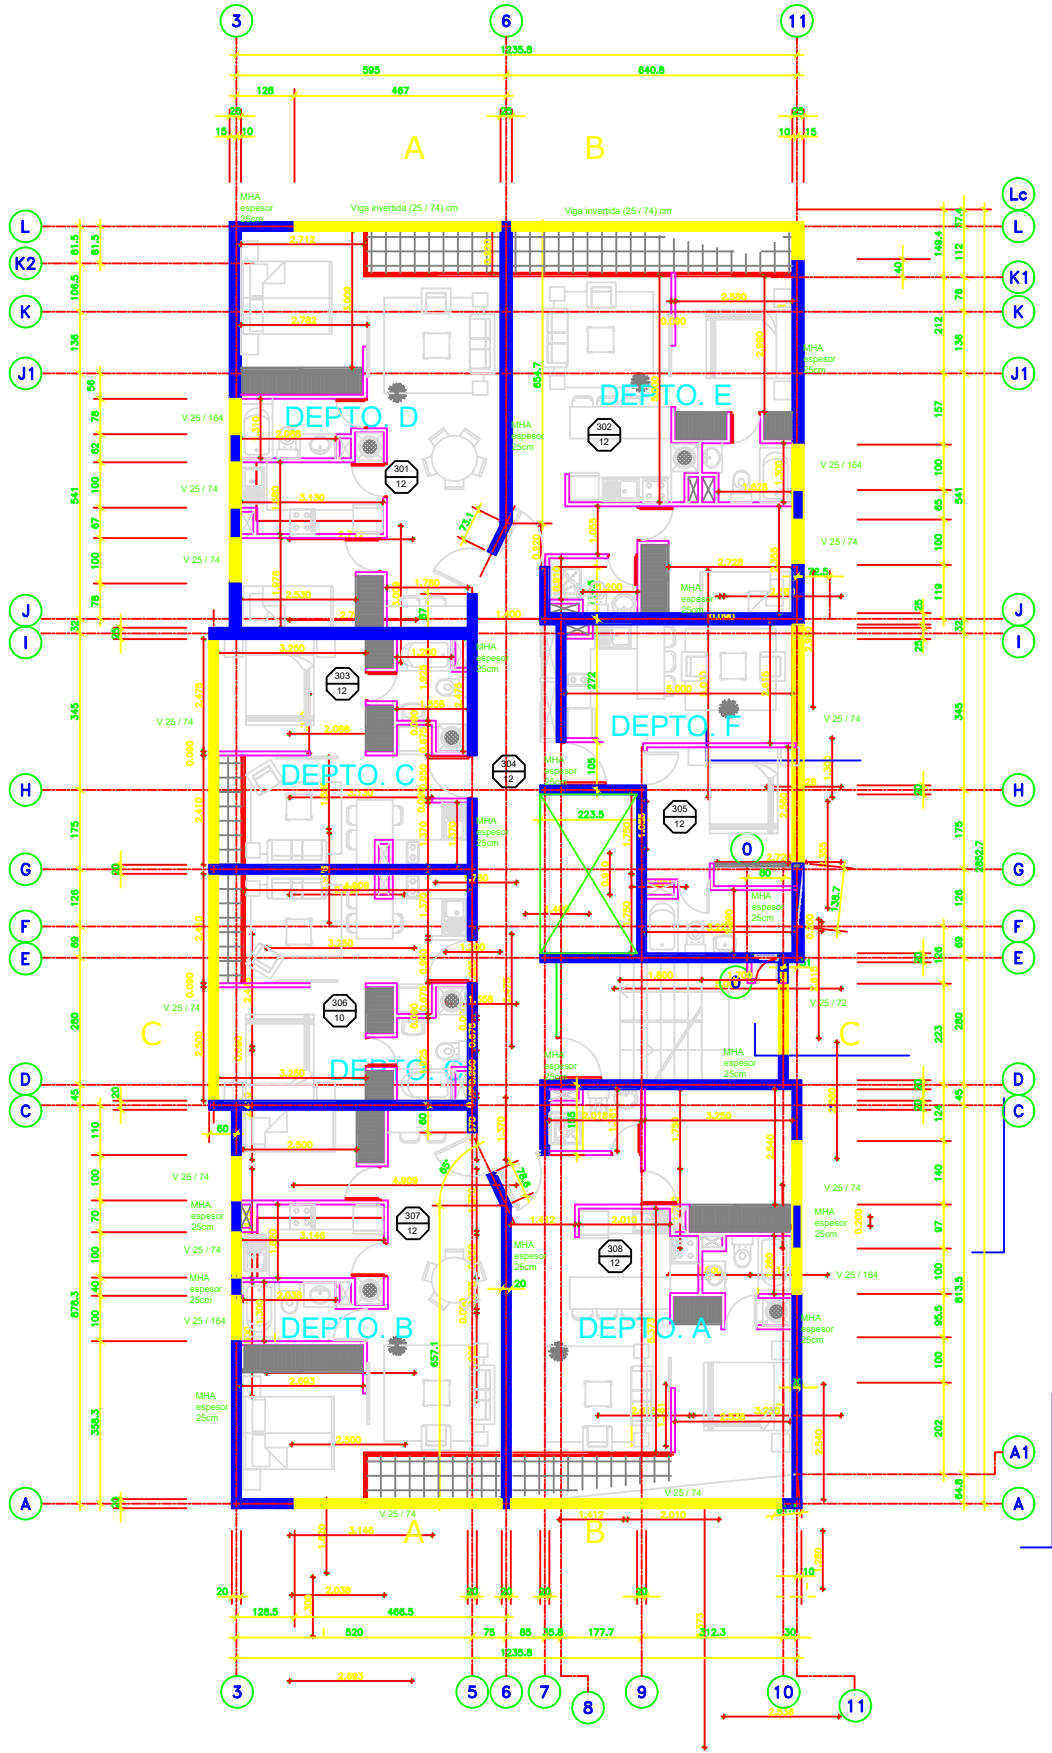

Universidad de los Andes FACULTAD DE INGENIERIA Y CIENCIAS APLICADAS		TRABAJO 2: ESTRUCTURACIÓN Y PRECÁLCULO SÍSMICO PLANOS DE ESTRUCTURACION Planos de: Planta Piso 3° - tipo		REVISIÓN	FECHA	DESCRIPCIÓN DE LA REVISIÓN
PROYECTO CIVIL 202610-6102				A	15/04/2026	Para revisión de profesor
Proyectó: Grupo 1	Fecha: Abril 2026					
PLANO N°4 DE 4						
		NUMERO DIBUJO T_A - 01	REV. A			